উপজেলা আক্কেলপুর	সহকারী সেটেলমেন্ট অফিসার মো: সোলায়মান আলী	উপ-সহকারী সেটেলমেন্ট অফিসার মো: হামিদ প্রধান	সরদার আমিন মো: আজিজুর রহমান	খানাপুরী কাজ বুঝার্ত আরম্ভ তাং ১১-৫-৯১ শেষ তাং ৩১-৫-৯১	মন্তব্য।

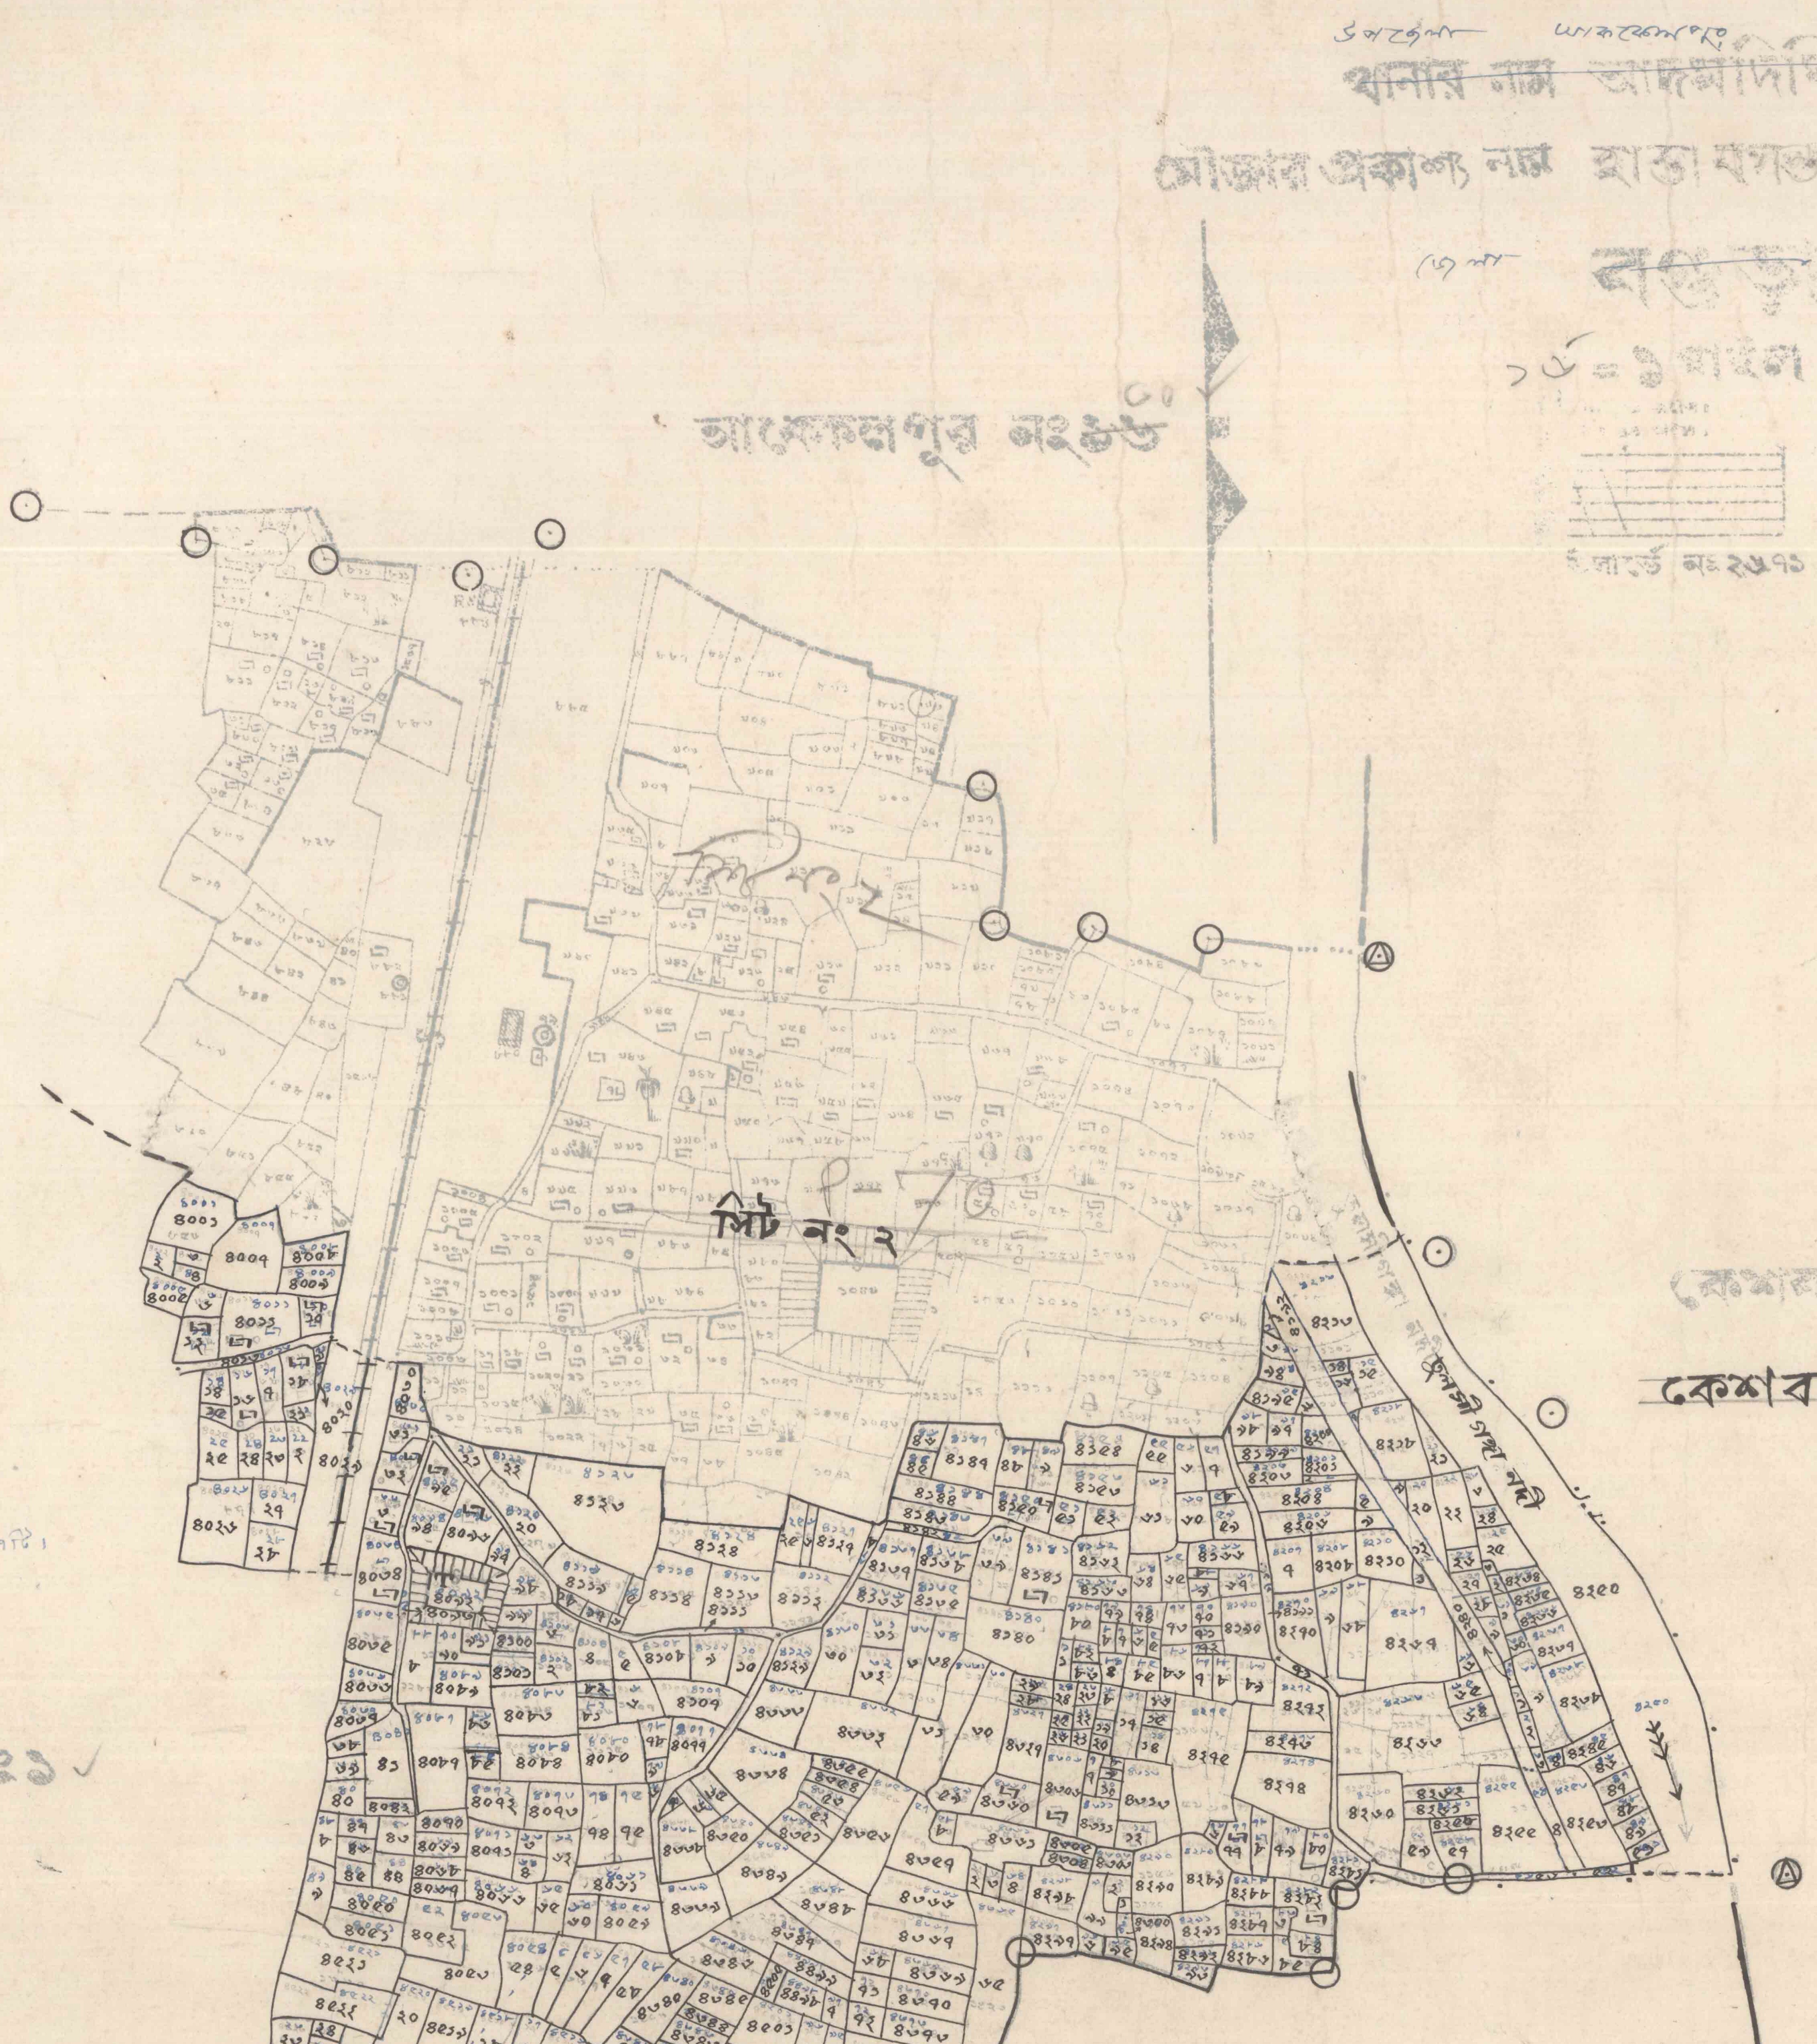

উপজেলা আক্কেলপুর

মৌজা হাস্তাবসন্তপুর

জে, এল, নং - ১৮

সিট নং - ৩

জিলা জয়পুরহাট

রে: সা: নং - ২৬৭১

স্কেল ১৬" = ১ মাইল

১০০ লিঙ্কে এক চেইন
৮০ চেইনে এক মাইল

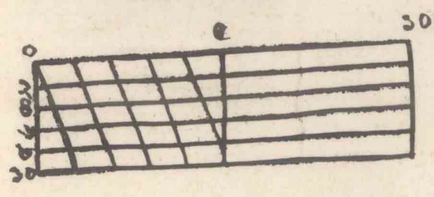

সাঙ্কেতিক

দালান	▨
ত্রিসীমানার পিলার ...	△
অন্যান্য পিলার ...	⊡
লোহার পিলার ...	+
ট্রাভার্স স্টেশন নূতন	⊙
ট্রাভার্স স্টেশন পুরাতন	⊙
জি, টি, স্টেশন ...	△
বেঞ্চ মার্ক	⌂
পাকা ইন্দারা ...	◎
নলকূপ	⊕
পান বরজ	▩

দাগ নং

রাস্তা... ৪০১৮,৪০৭৮,৪১১১,৪১৯১,৪২৭২,৪২৫৪,৪২৬৭।
হালট ... ৪২৫২,৪২৫৩,৪২৭১।
খাল/নদী ... ৪২৫০,
অত্র সিট ভুক্ত...৪০০১–৪৫৪৫,৪৫৪৭–৪৭৫৭
ছুট দাগ ... ৪৫৪৬।
বাটা দাগ... x
রেল রাস্তা ... ৪০২৯।

সরকার কর্তৃক প্রদত্ত ক্ষমতাবলে ১৯৯১ – ২০০৫ সনে প্রস্তুত
মো: মহসিন আলী খান
সেটেলমেন্ট অফিসার এবং সুপারিনটেনডেন্ট অব সার্ভে

MADE UNDER THE AUTHORITY OF GOVERNMENT IN
SETTLEMENT OFFICER AND ... OF SURVEY

... FOR THE PURPOSE OF ... UNDER CHAPTER IV OF THE E. B. S. A. & T. ACT, 1950, WITHOUT ...
SETTLEMENT OFFICER & SUPERINTENDENT OF SURVEY

অত্র সিটভুক্ত দাগ নং:
৪০০১ – ৪৫৪৫, ৪৫৪৭ – ৪৭৫৭
ছুটদাগ = ৪৫৪৬

চিহ্ন:
রাস্তা = ৪০১৮, ৪০৭৮, ৪১১১, ৪১৯১, ৪২৭২, ৪২৫৪, ৪২৬৭,
হালট = ৪২৫২, ৪২৫৩, ৪২৭১,
রেল লাইন: ৪০২৯,
নদী: ৪২৫০