উপ জেলা সহকারী অফিসার নাম	থানা হুবী কামবুকারক আমিনের নাম	কাজ আরম্ভ	কাজের শেষ
মোঃ আজিজুর রহমান	মোঃ রুহুল আমিন, সরদার আমিন	১৭-২-৮৭ ইং	১৮-৪-৮৭ ইং

থানা আক্কেলপুর

উপজেলার নাম আক্কেলপুর

মৌজা চিয়ারীগ্রাম

মৌজার নাম চিয়ারী গ্রাম নং ৯৫ সিট নং ২

জে, এল, নং ১০৪

সিট নং- ১

জিলা জয়পুরহাট

জিলা জয়পুরহাট

রেঃ সাঃ নং- ৩০

স্কেল ১৬″ = ১ মাইল

১০০ লিংকে এক চেইন

৮০ চেইনে এক মাইল

১০ চেইন

সাঙ্কেতিক

দালান	▬
ত্রিসীমানার পিলার	△
লোহার পিলার	⫯
অন্যান্য পিলার	▣
ট্রাভার্স স্টেশন নতুন	⊙
ট্রাভার্স স্টেশন পুরাতন	⊙
জি, টি, স্টেশন	▲
বেঞ্চমার্ক	⍊
ইন্দারা	◎
নলকূপ	⊕
পানবরজ	▭

দাগ নং

পাকা রাস্তা ... ×

কাঁচা রাস্তা ... ১০৮২, ১১০৪, ১১৬৬, ১৬৫৭,

খাল ... ×

অত্র সিটভুক্ত ... ১–১৬৬০

কাটা দাগ ... ১৪৯৭/১৬৫৭, ৯৯০/১৬৫৮, ৯৯১/১৬৫৯, ৯৯৩/১৬৬০,

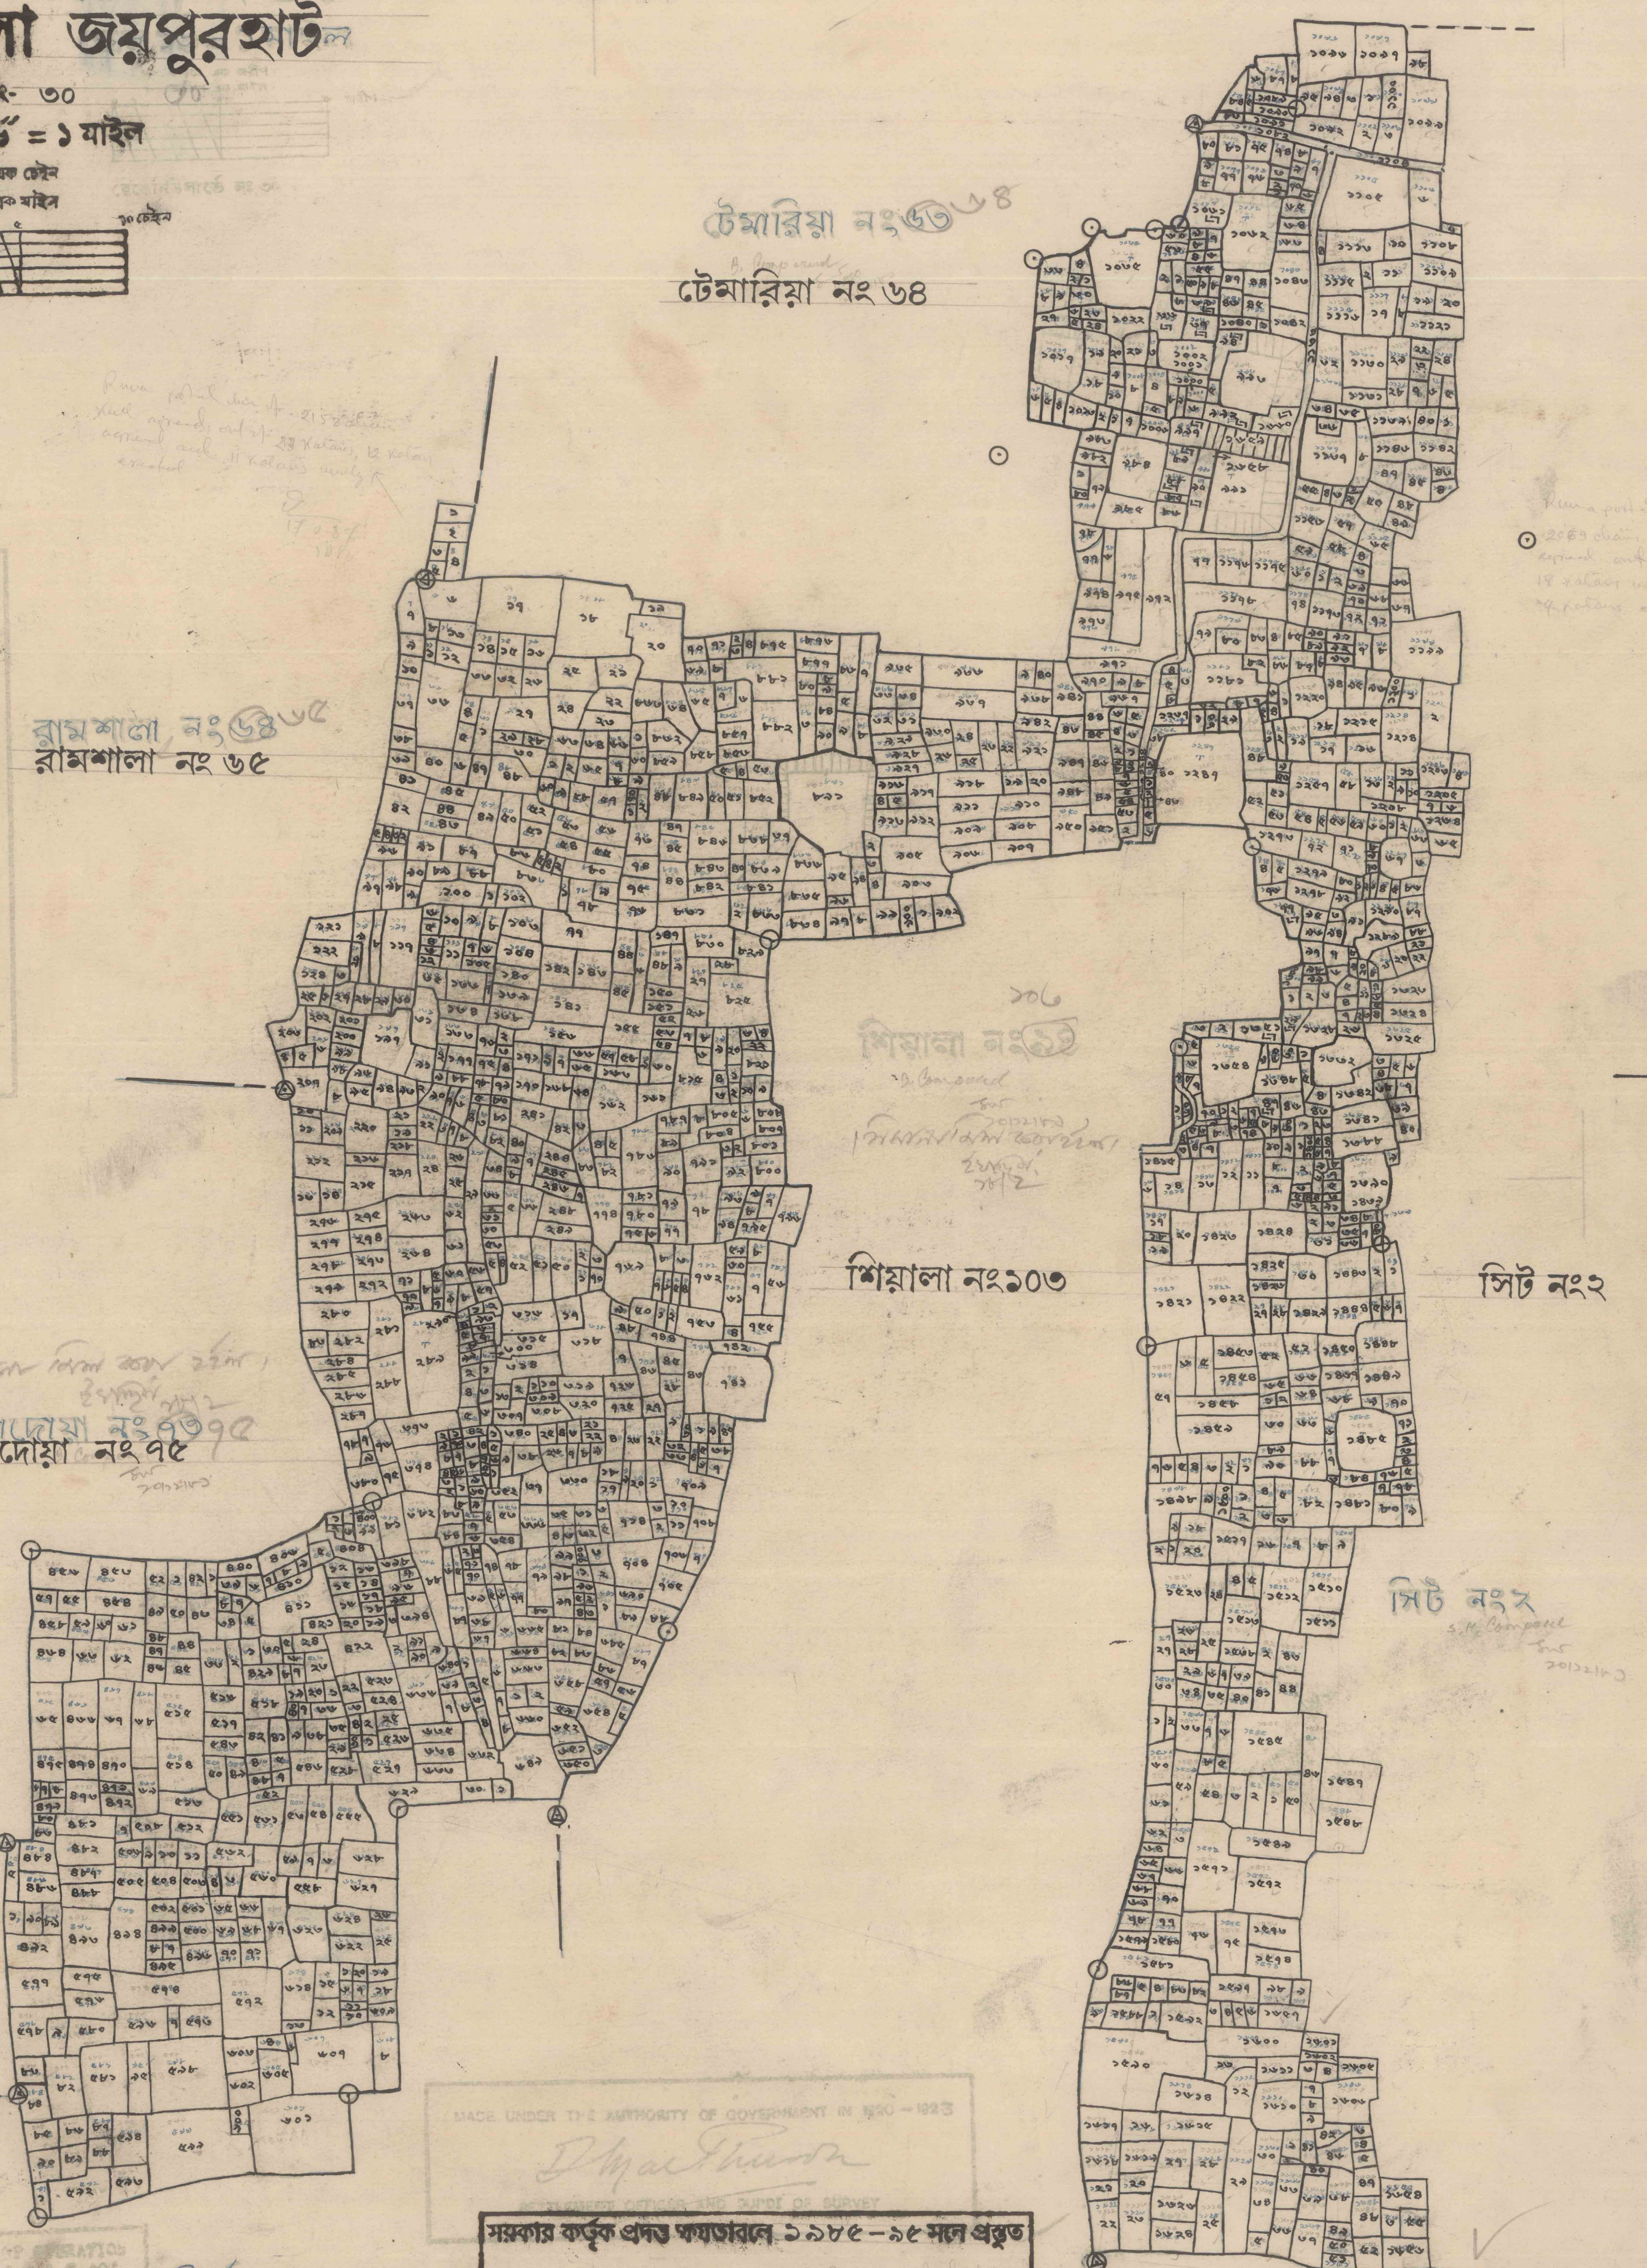

Rume partal lived 2407 chains
Null agreed out of 30 Kalam
14 Kalam agreed at the next 16 K...
newly erected

17-8-87

MADE UNDER THE AUTHORITY OF GOVERNMENT IN 1920 – 1923

D. MacPherson

SETTLEMENT OFFICER AND SUPDT OF SURVEY

ADOPTED FOR THE [illegible] OPERATION UNDER CHAPTER IV OF THE [illegible], 1990, WITHOUT CORRECTION.

SETTLEMENT OFFICER & SUPERINTENDENT OF SURVEY.

সরকার কর্তৃক প্রদত্ত ক্ষমতাবলে ১৯৮৫–৯৫ সনে প্রস্তুত

মুঃ : [illegible]

সেটেলমেন্ট অফিসার এবং সুপারিনটেনডেন্ট অব সার্ভে

১) কাঁচা রাস্তা ১০৮২, ১১০৪, ১১৬৬, ১৬৫৭,-

২) পাকা — ×

৩) খাল — ×

৪) নদী ×

অত্র সিট ভুক্ত দাগ

১ – ১৬৬০

পাঃ ইঃ — ×

সংখ্যা —

মোট — দাগ — ১৬৬০

২৮/৪/৯৪