থানা আক্কেলপুর
মৌজা চক রঘুনাথ
জে, এল, নং - ২০
সিট নং - x

জিলা জয়পুর হাট

রেঃ সাঃ নং - ২৬৫১ - ২৬৫৫
স্কেল ১৬" = ১ মাইল

১০০ লিঙ্কে এক চেইন
৮০ চেইনে এক মাইল

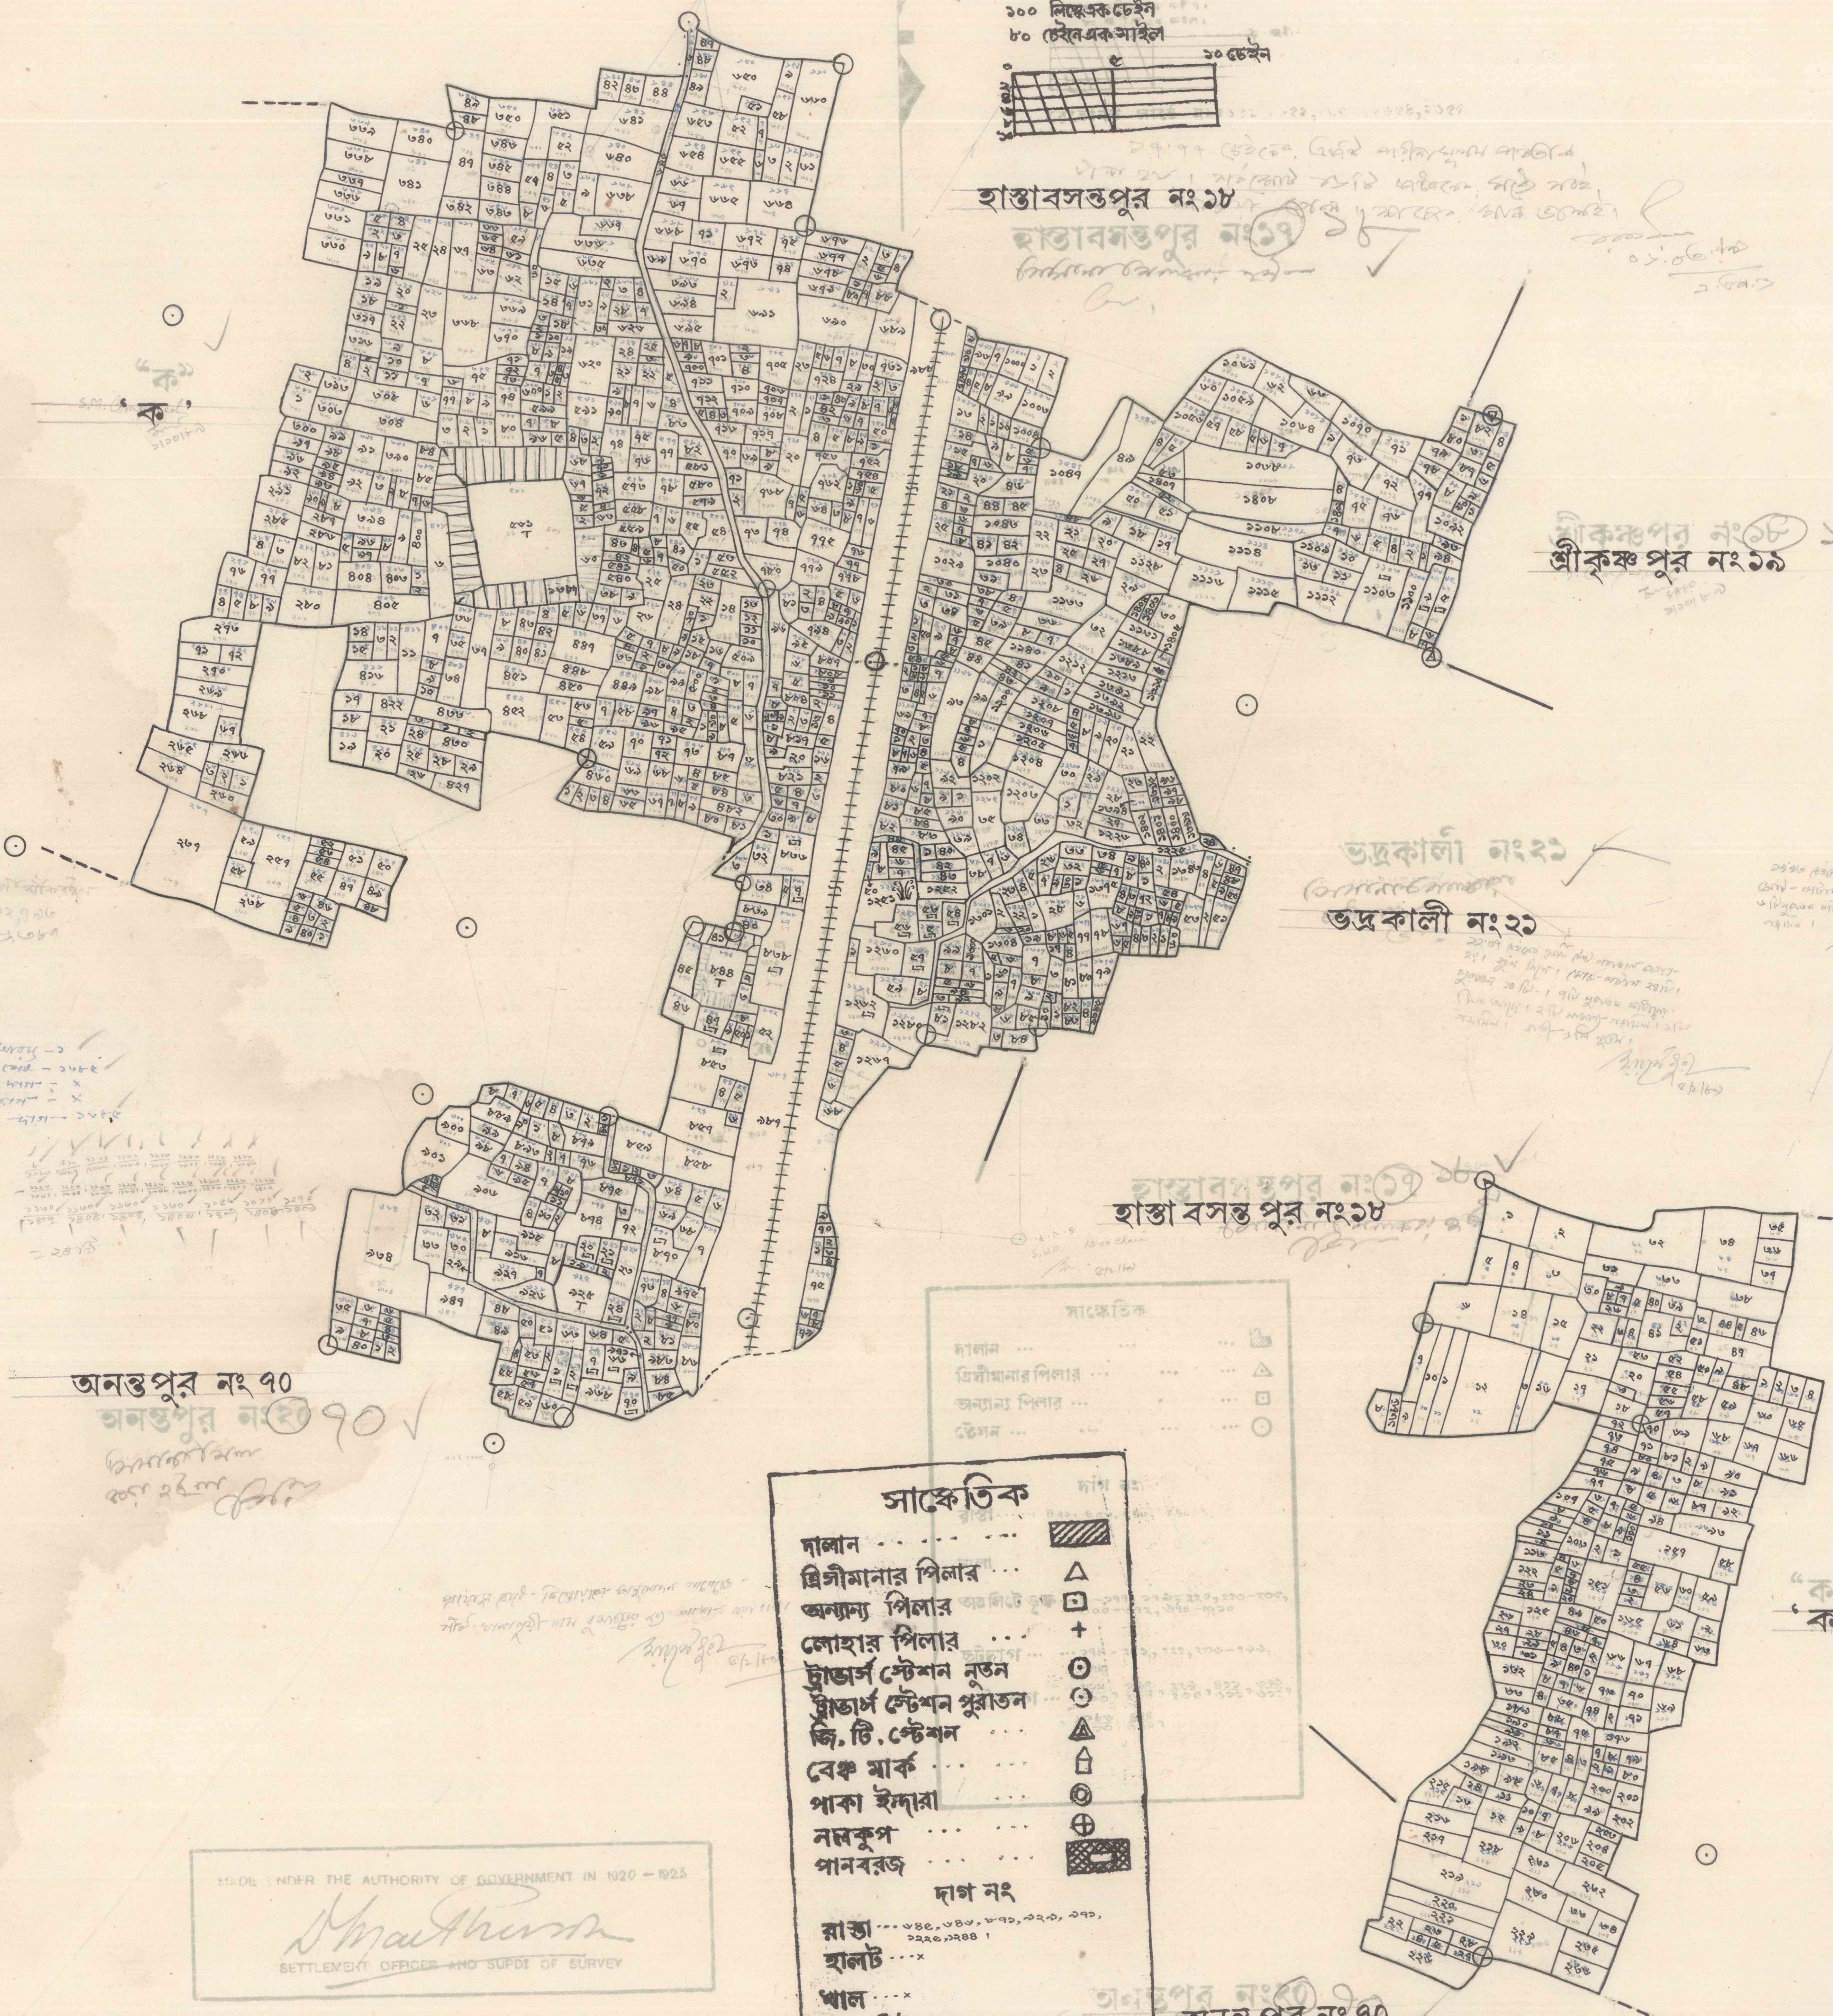

সাঙ্কেতিক

দালান ...	▨
ত্রিসীমানার পিলার ...	△
অন্যান্য পিলার	⊡
লোহার পিলার ...	+
ট্রাভার্স স্টেশন নূতন	⊙
ট্রাভার্স স্টেশন পুরাতন	⊙
জি. টি. স্টেশন ...	▲
বেঞ্চ মার্ক ...	⌂
পাকা ইন্দারা ...	◎
নলকূপ ...	⊕
পানবরজ ...	▩

দাগ নং

রাস্তা ... ৬৪৫, ৬৪৬, ৮৭১, ৯২৯, ৯৭১, ১২২৫, ১২৪৪।
হালট ... x
খাল ... x
অত্র সিট ভুক্ত ... ১ - ১৪০৯।
ছুট দাগ ... x
বাটা দাগ ... $\frac{৮}{১৩৮৬}$, $\frac{৫৭০}{১৩৮৭}$, $\frac{১১৩২}{১৩৮৮}$, $\frac{১১৩১}{১৩৮৯}$, $\frac{১২১৩}{১৩৯০}$, $\frac{১২১৩}{১৩৯১}$, $\frac{১২১৩}{১৩৯২}$, $\frac{১২১৩}{১৩৯৩}$, $\frac{১২২৩}{১৩৯৪}$, $\frac{১২২৩}{১৩৯৫}$, $\frac{১২২৩}{১৩৯৬}$, $\frac{১২২৩}{১৩৯৭}$, $\frac{১২২৩}{১৩৯৮}$, $\frac{১২২৩}{১৩৯৯}$, $\frac{১২২৩}{১৪০০}$, $\frac{১২২৩}{১৪০১}$, $\frac{১২২৩}{১৪০২}$, $\frac{১১৩০}{১৪০৩}$, $\frac{১১৩০}{১৪০৪}$, $\frac{১১৩০}{১৪০৫}$, $\frac{১১৩০}{১৪০৬}$, $\frac{১০৫৩}{১৪০৭}$, $\frac{১০৫৮}{১৪০৮}$, $\frac{১০৭৪}{১৪০৯}$।

MADE UNDER THE AUTHORITY OF GOVERNMENT IN 1920 – 1923
SETTLEMENT OFFICER AND SUPDT OF SURVEY

ADOPTED FOR THE PURPOSE OF OPERATION UNDER CHAPTER IV OF THE E.B.S.A.& T. ACT, 1950, WITHOUT CORRECTION.
SETTLEMENT OFFICER & SUPERINTENDENT OF SURVEY

সরকার কর্তৃক প্রদত্ত ক্ষমতাবলে ১৯৮৯-৯৮ সনে প্রস্তুত
মোঃ মহসীন খালী সরদার
বীঃ প্রতীক
সেটেলমেন্ট অফিসার এবং সুপারিনটেনডেন্ট অব সার্ভে

২৭৫১, ২৭৫২, ২৭৫৩, ২৭৫৪, ২৭৫৫,

রাস্তা :— ৬৪৫, ৬৪৬, ৮৭১, ৯২৯, ৯৭১, ১২২৫, ১২৪৪
খাল :— x
হালট :— x

চূড়ান্ত পরীক্ষায়
০৬/১০/৯৮

হস্তলিখন :— চিত্তরঞ্জন বিশ্বাস।
০৬/১০/৯৮