উপজেলা	ভারপ্রাপ্ত সহকারী সেটেলমেন্ট অফিসার	উপ-সহকারী সেটেলমেন্ট অফিসার	সর্দার আমিন	খানাপুরী কাজ শুরু ও শেষ	মন্তব্য
আক্কেলপুর	মোঃ সোলায়মান আলী	আবুল মান্নান	বিজয় চন্দ্র দাস	শুরু তাং ১০-৫-৯০ শেষ তাং ৩১-৫-৯০	

মৌজার প্রকাশ্য নাম রোয়ার নং:৮ সিট নং২

উপজেলা - আক্কেলপুর
মৌজা - রোয়ার
জে, এল, নং - ৮
সিট নং - ২

জিলা - জয়পুরহাট

রেঃ সাঃ নং - ২৬৮৫, ২৬৮৮, ২৬৮৯
স্কেল ১৬" = ১ মাইল

১০০ লিঙ্কে এক চেইন
৪০ চেইনে এক মাইল

০ ৫ ১০চেইন

দাগ আরম্ভ - ৪০০১
দাগ শেষ - ৪৫৭৭
ছুট দাগ - ৪৫৮০ = ১
বাটা দাগ - ৪৬৬৬/৪৫৭৮ = ১
মোট দাগ - ৫৭৭

সাঙ্কেতিক

দালান	▨
ত্রিসীমানার পিলার ...	△
অন্যান্য পিলার ...	⊡
লোহার পিলার ...	+
ট্রাভার্স স্টেশন নূতন	⊙
ট্রাভার্স স্টেশন পুরাতন	⊙
জি, টি, স্টেশন ...	◬
বেঞ্চ মার্ক	⌂
পাকা ইন্দারা ...	◎
নলকূপ	⊕
পানবরজ	▩

দাগ নং

রাস্তা ... ৪০৩৫, ৪১৭৭, ৪২১৪, ৪২২৮, ৪২৭৩, ৪৩০৭, ৪৩২৫, ৪৩৬২, ৪৬৫৩, ৪৫৭৭.
হালট ... x
খাল ... x
অত্র সিট ভুক্ত ... ৪০০১ — ৪৫৫৯, ৪৫৬১ — ৪৫৭৮.
ছুট দাগ ... ৪৫৮০.
বাটা দাগ ... ৪৬৬৬/৪৫৭৮.

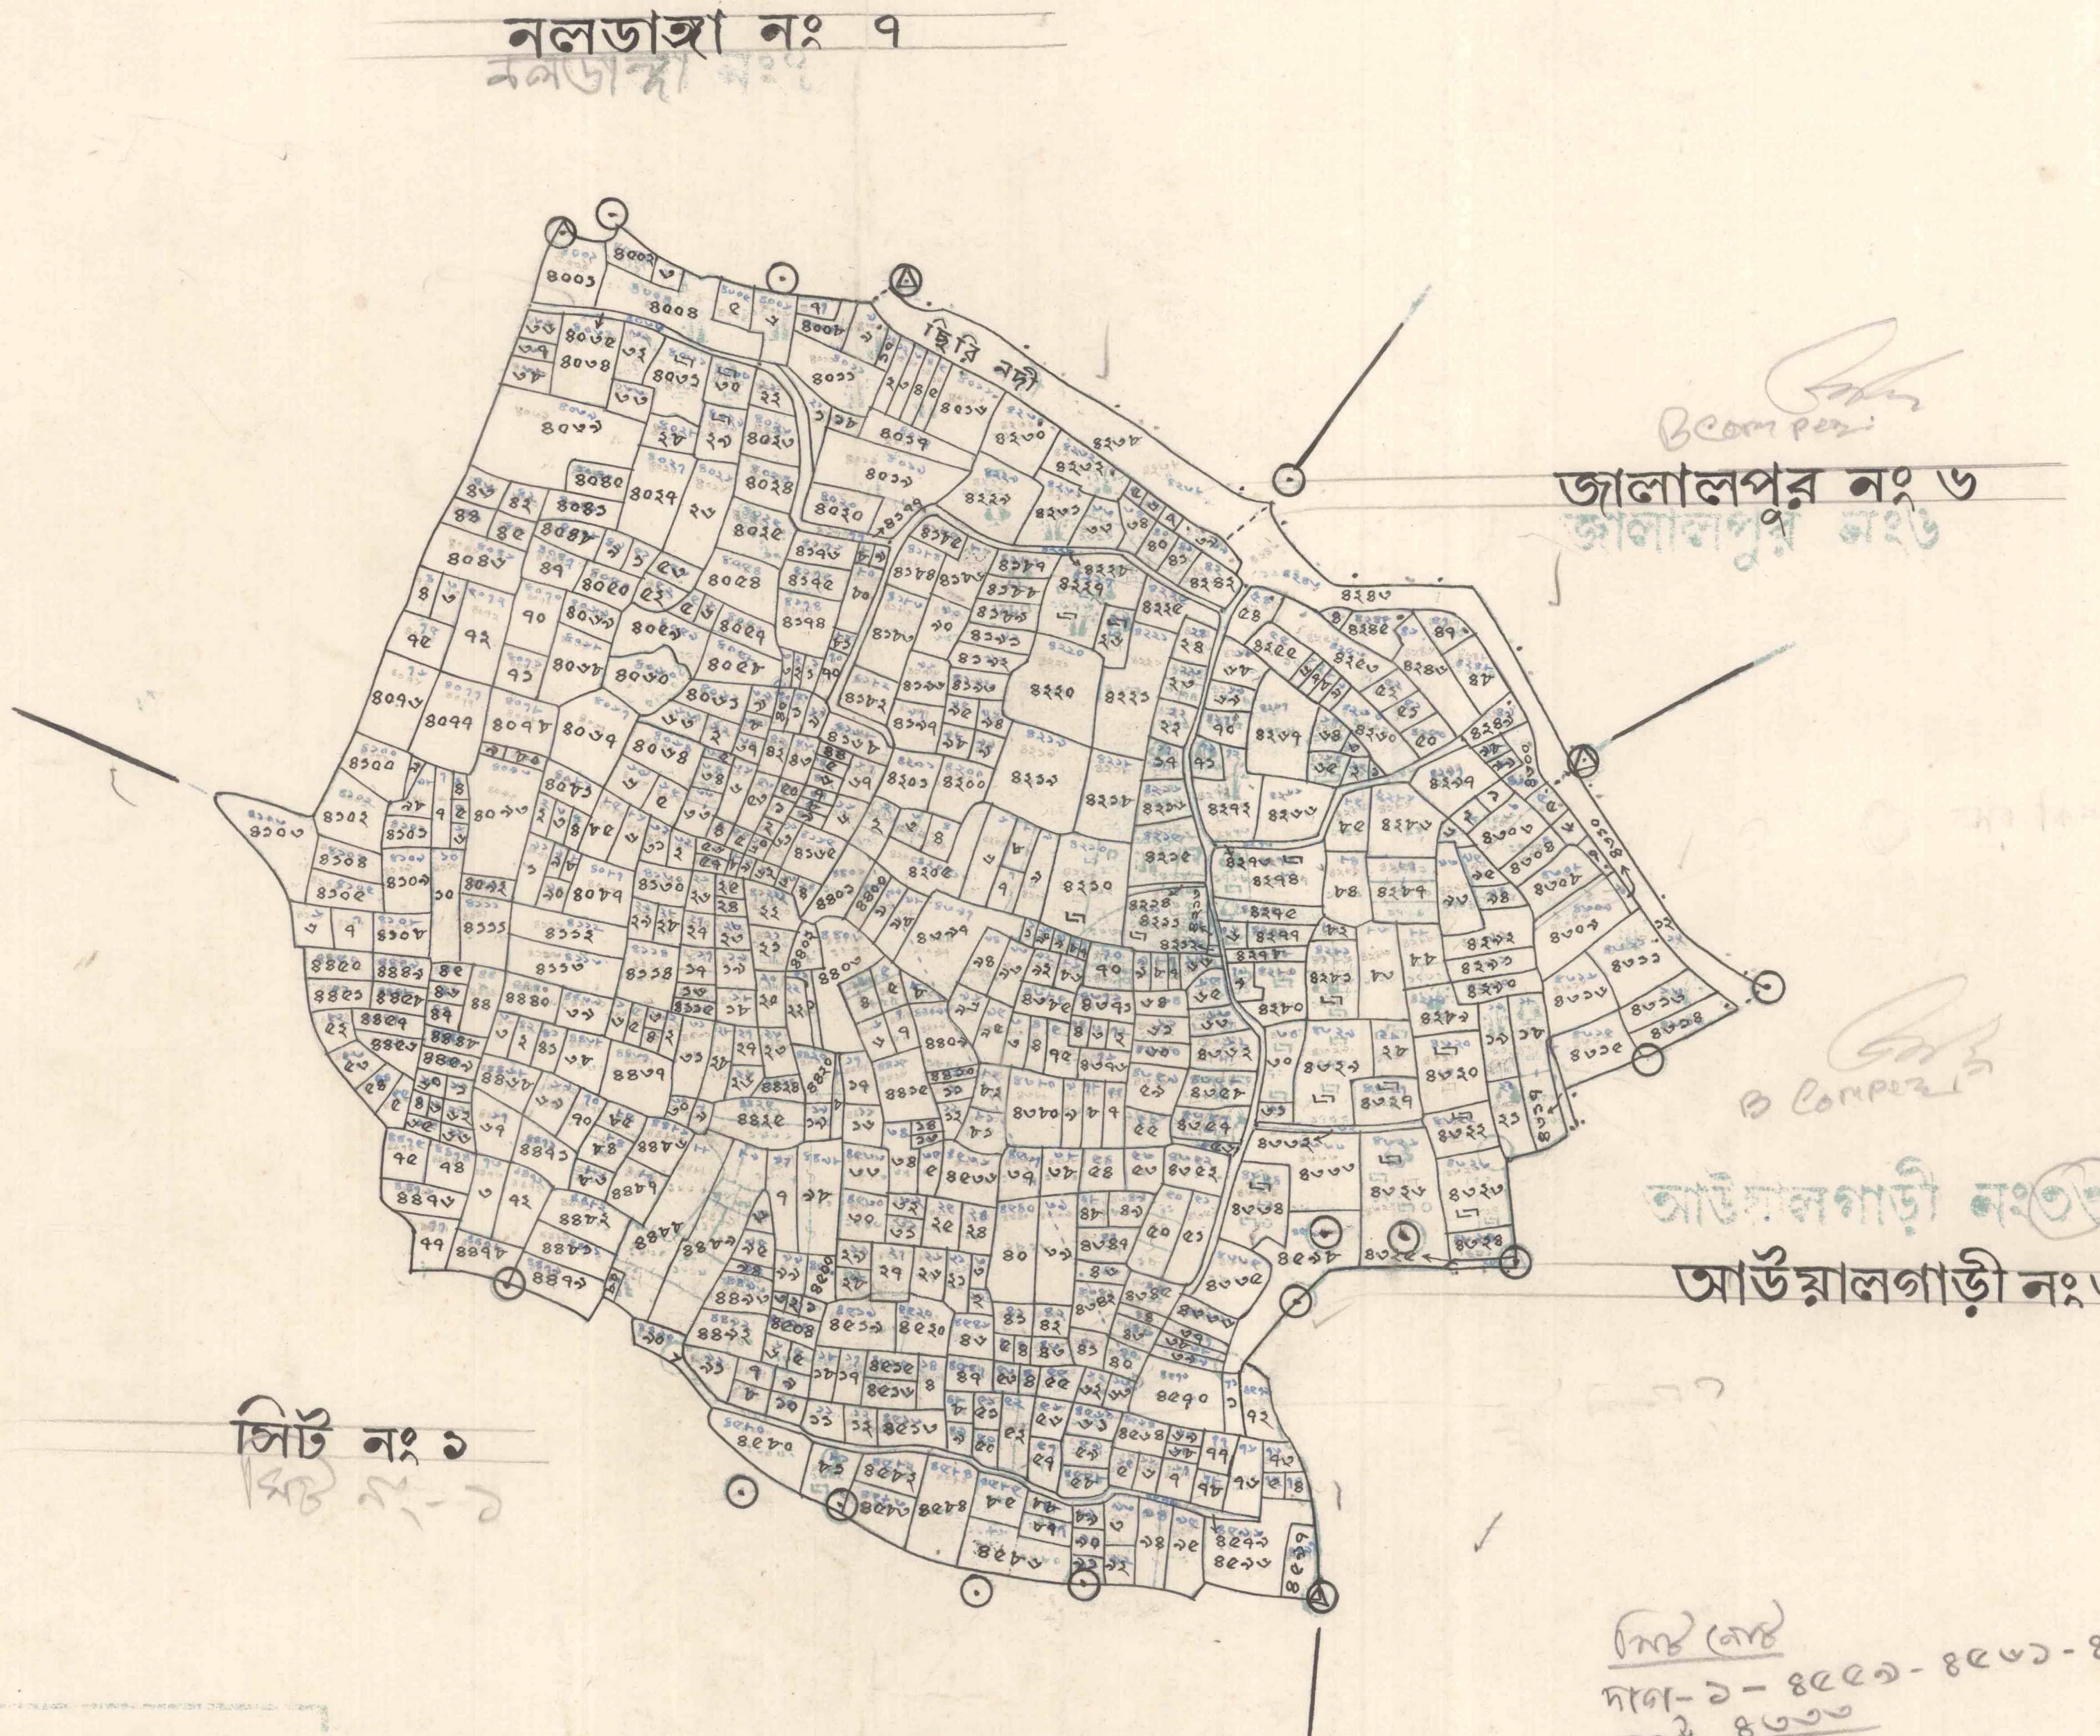

সিট নোট
দাগ - ১ - ৪৫৫৯ - ৪৫৬১ - ৪৫৭৮
বাটা ৪৬৬৬/৪৫৭৮
রাস্তার - ৪০৩৫, ৪১৭৭, ৪২১৪, ৪২২৮, ৪২৭৬, ৪৩০৭, ৪৩২৫, ৪৩৬২, ৪৬৫৩, ৪৫৭৭,
সমন্বয় ও অনুমোদন
28/02/08

সরকার কর্তৃক প্রদত্ত ক্ষমতা বলে ১৯৯০-২০০৪ সনে প্রস্তুত

সেটেলমেন্ট অফিসার এবং সুপারিনটেনডেন্ট অব সার্ভে